



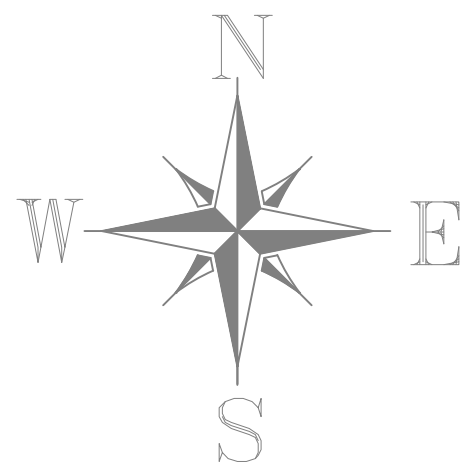

GEOREFERENCIACION					
NAME	NORTE	ESTE	ELEVACION	WGS84 LATITUDE	WGS84 LONGITUDE
GPS1	93123.589	92086.807	2806.199	4°32'02.65451"N	74°08'55.77427"W
GPS2	93138.894	92075.039	2806.856	4°32'03.15259"N	74°08'56.15591"W

CUADRO DE MOJONES Y AREA		
MOJON	NORTE	ESTE
1	93140.65	92071.00
2	93142.03	92074.83
3	93143.40	92078.65
4	93144.26	92081.03
5	93145.63	92084.86
6	93147.01	92088.69
7	93135.61	92091.52
8	93134.77	92087.53
9	93133.93	92083.54
10	93133.44	92081.08
11	93132.64	92077.09
12	93131.85	92073.09
13	93126.98	92074.25
14	93128.58	92082.26
15	93129.08	92084.72
16	93130.74	92092.72
17	93125.88	92093.93
18	93124.22	92085.90
19	93123.72	92083.44
20	93122.12	92075.41
21	93117.26	92076.57
22	93118.87	92084.62
23	93119.36	92087.09
24	93121.02	92095.14
25	93116.16	92096.35
26	93114.50	92088.27
27	93114.01	92085.81
28	93112.39	92077.73
29	93107.53	92078.88
30	93109.15	92086.99
31	93109.64	92089.45
32	93111.29	92097.55
33	93106.43	92098.76
34	93104.78	92090.63
35	93104.29	92088.17
36	93102.66	92080.04
37	93097.8	92081.2
38	93099.43	92089.35
39	93099.93	92091.82
40	93101.57	92099.97
41	93096.71	92101.17
42	93095.07	92093
43	93094.57	92090.53
44	93092.94	92082.36
1	93140.65	92071

CUADRO DE AREAS LOTEO PREDIOS CL 81C SUR # 18N-05		
PREDIO	AREA M2	MOJONES
AREA GENERAL	954.900	1,2,3,4,5,6,7,16,17,24,25,32,33,40,41,42,43,44,37,37,36,29,28,21,13,12,1
L1	37.920	1,2,11,12,1
L2	40.360	2,3,10,11,2
L3	44.270	4,5,8,9,4
L4	46.560	5,6,7,8,5
1.000	40.730	12,11,10,14,13,12
2.000	40.850	13,14,19,20,13
3.000	40.980	20,19,22,21,20
4.000	41.100	21,22,27,28,21
5.000	41.230	28,27,30,29,28
6.000	41.350	29,30,35,36,29
7.000	41.480	36,35,38,37,36
8.000	41.600	37,38,43,44,37
9.000	40.830	9,8,7,16,15,9
10.000	40.940	15,16,17,18,15
11.000	41.060	18,17,24,23,18
12.000	41.170	23,24,25,26,23
13.000	41.290	26,25,32,31,26
14.000	41.410	31,32,33,34,31
15.000	41.520	34,33,40,39,34
16.000	41.640	39,40,41,42,39

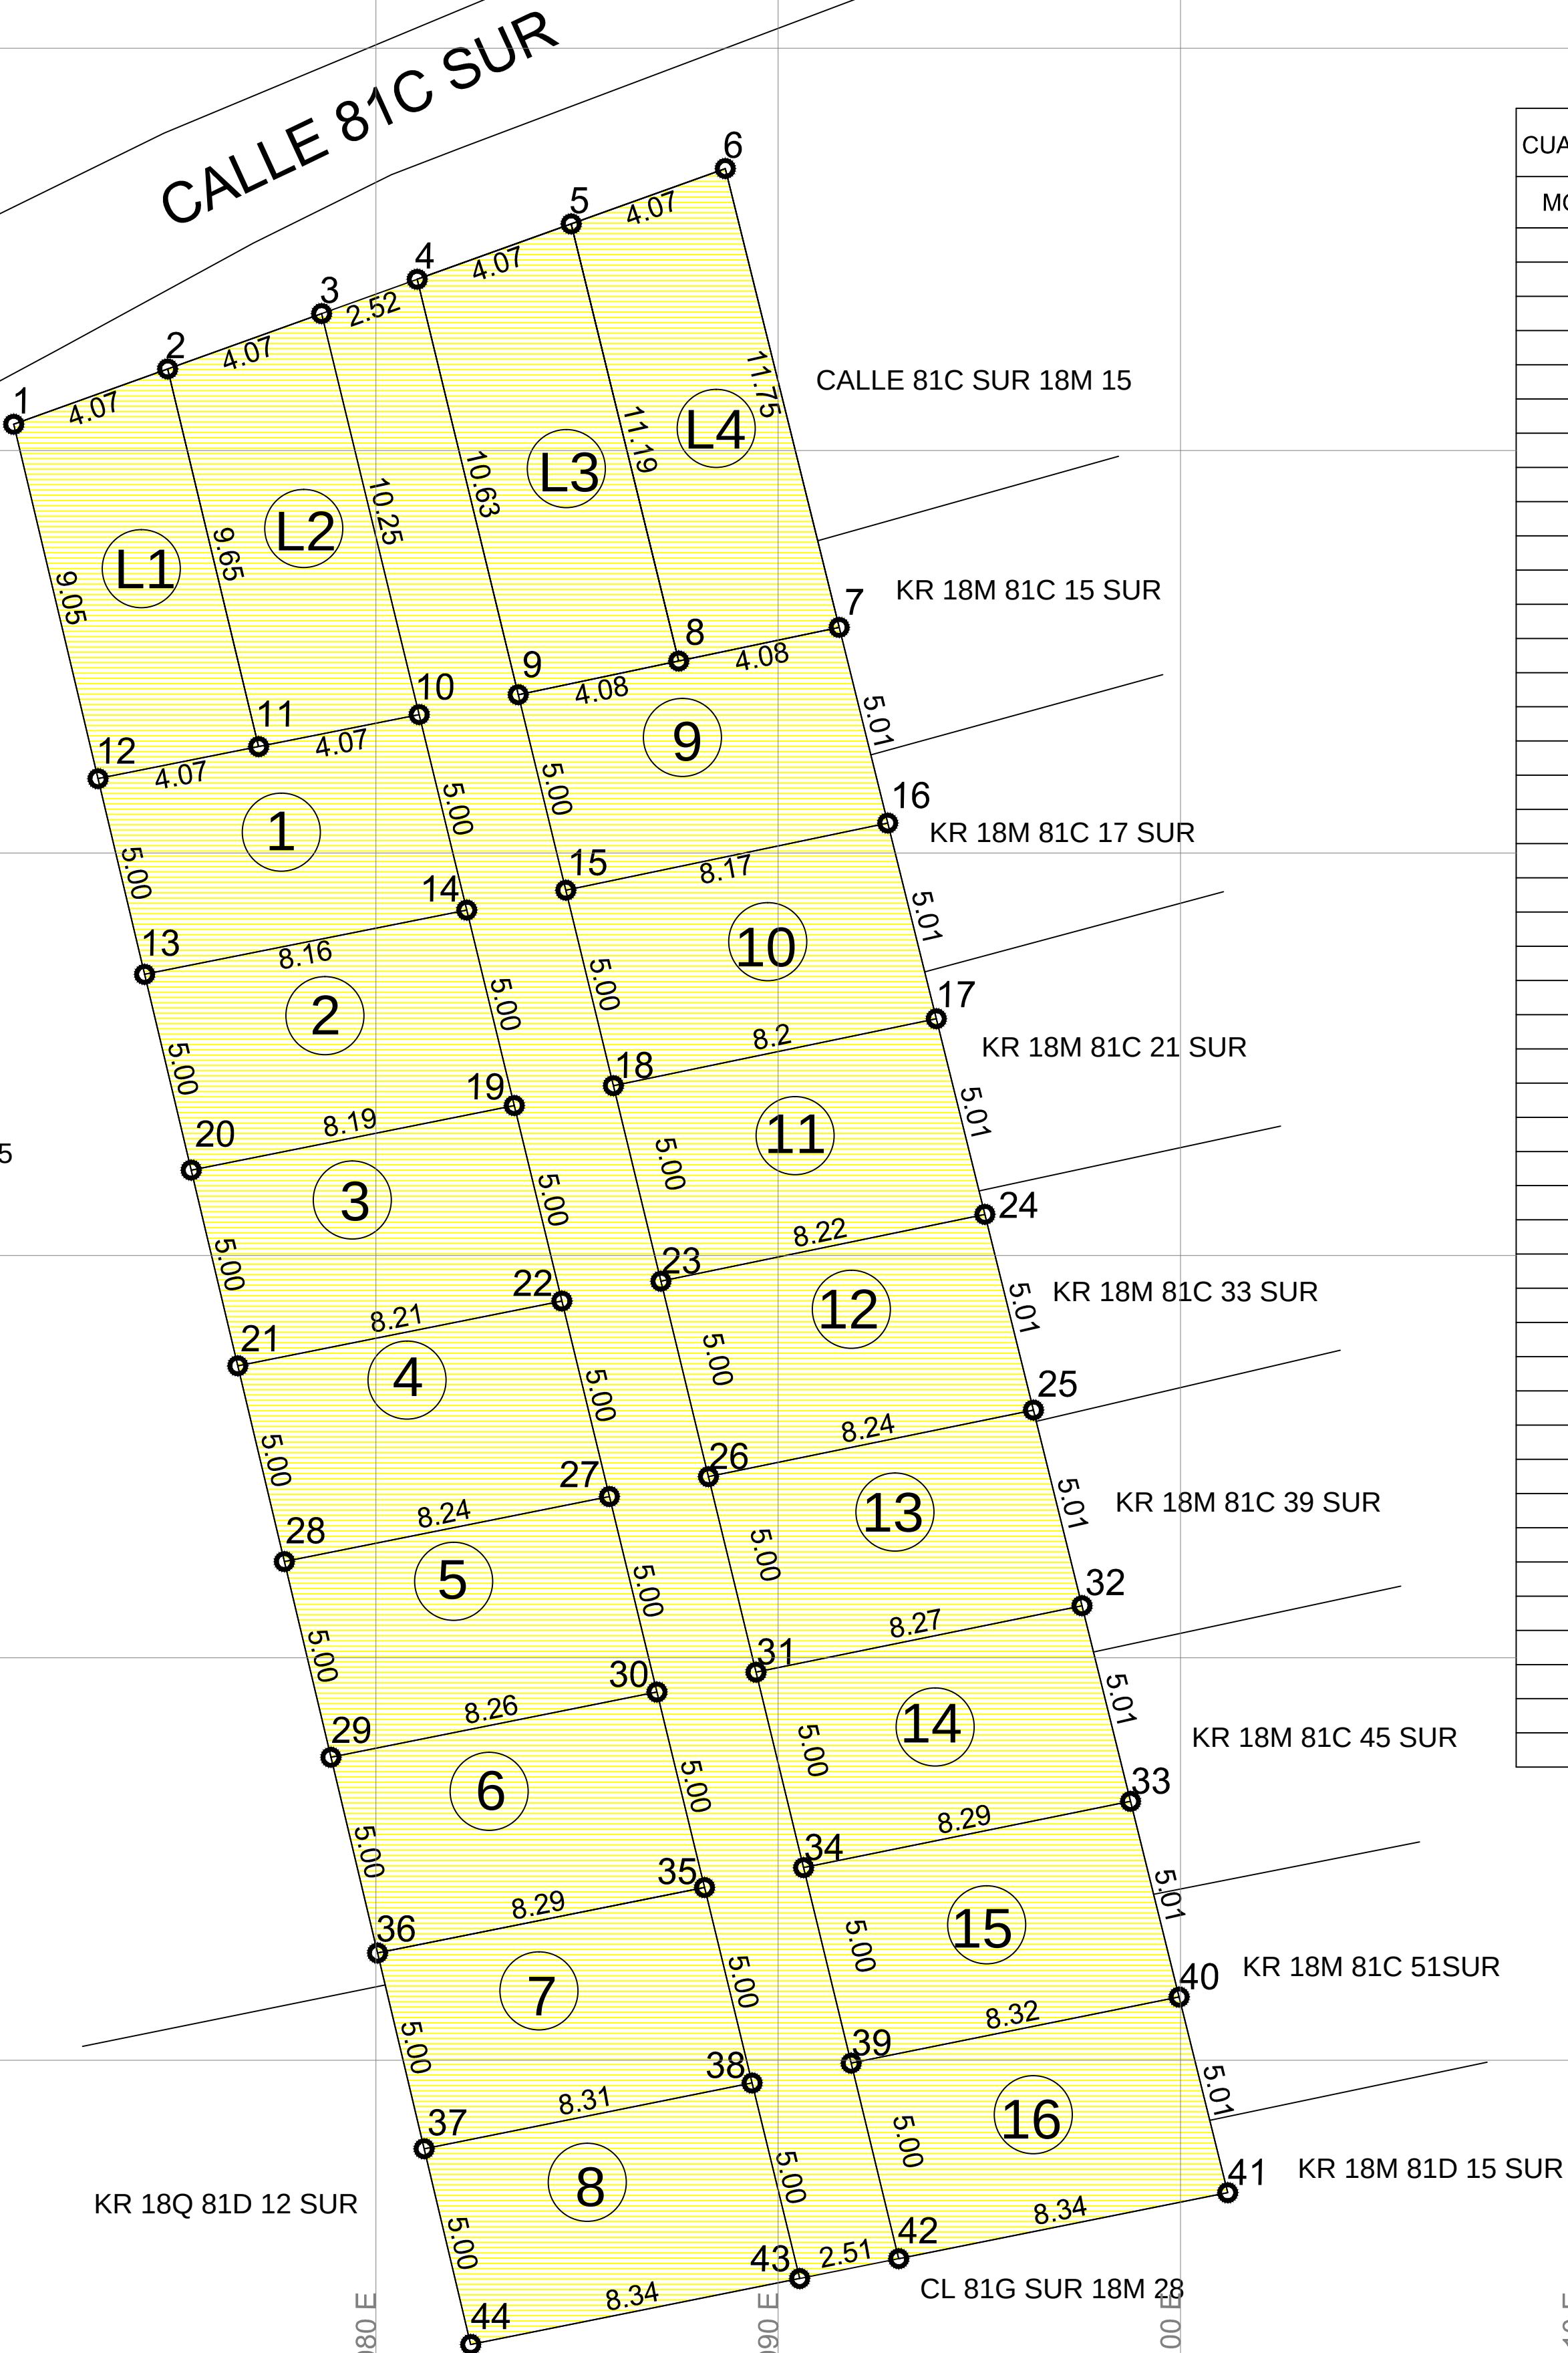


PROYECTO
LEVANTAMIENTO TOPOGRAFICO



LOTES
LOCALIDAD 19 CIUDAD BOLIVAR

CONJUNTO RESIDENCIAL
DAKARY DE ARABIA
CAL 81C SUR 18N 05
BARRIO ARABIA

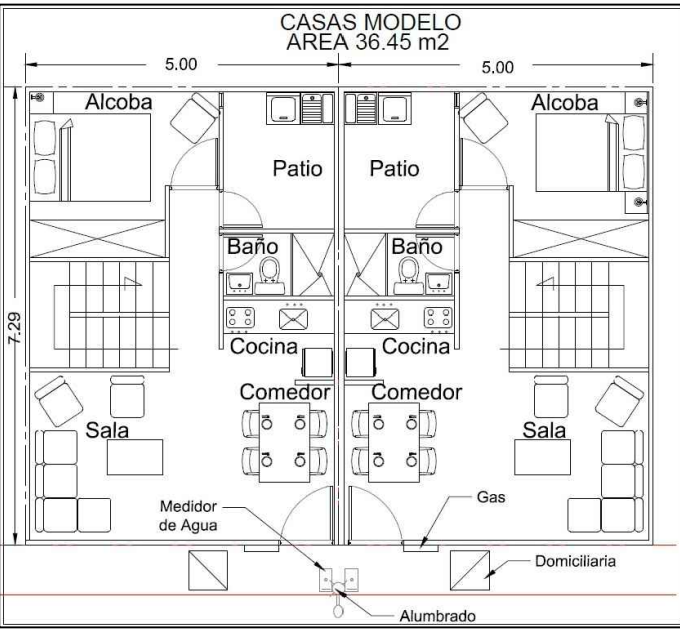

DIBUJO DAKARY ARABIA LOTE0

FECHA OCTUBRE DE 2025

ESCALA 1:125